


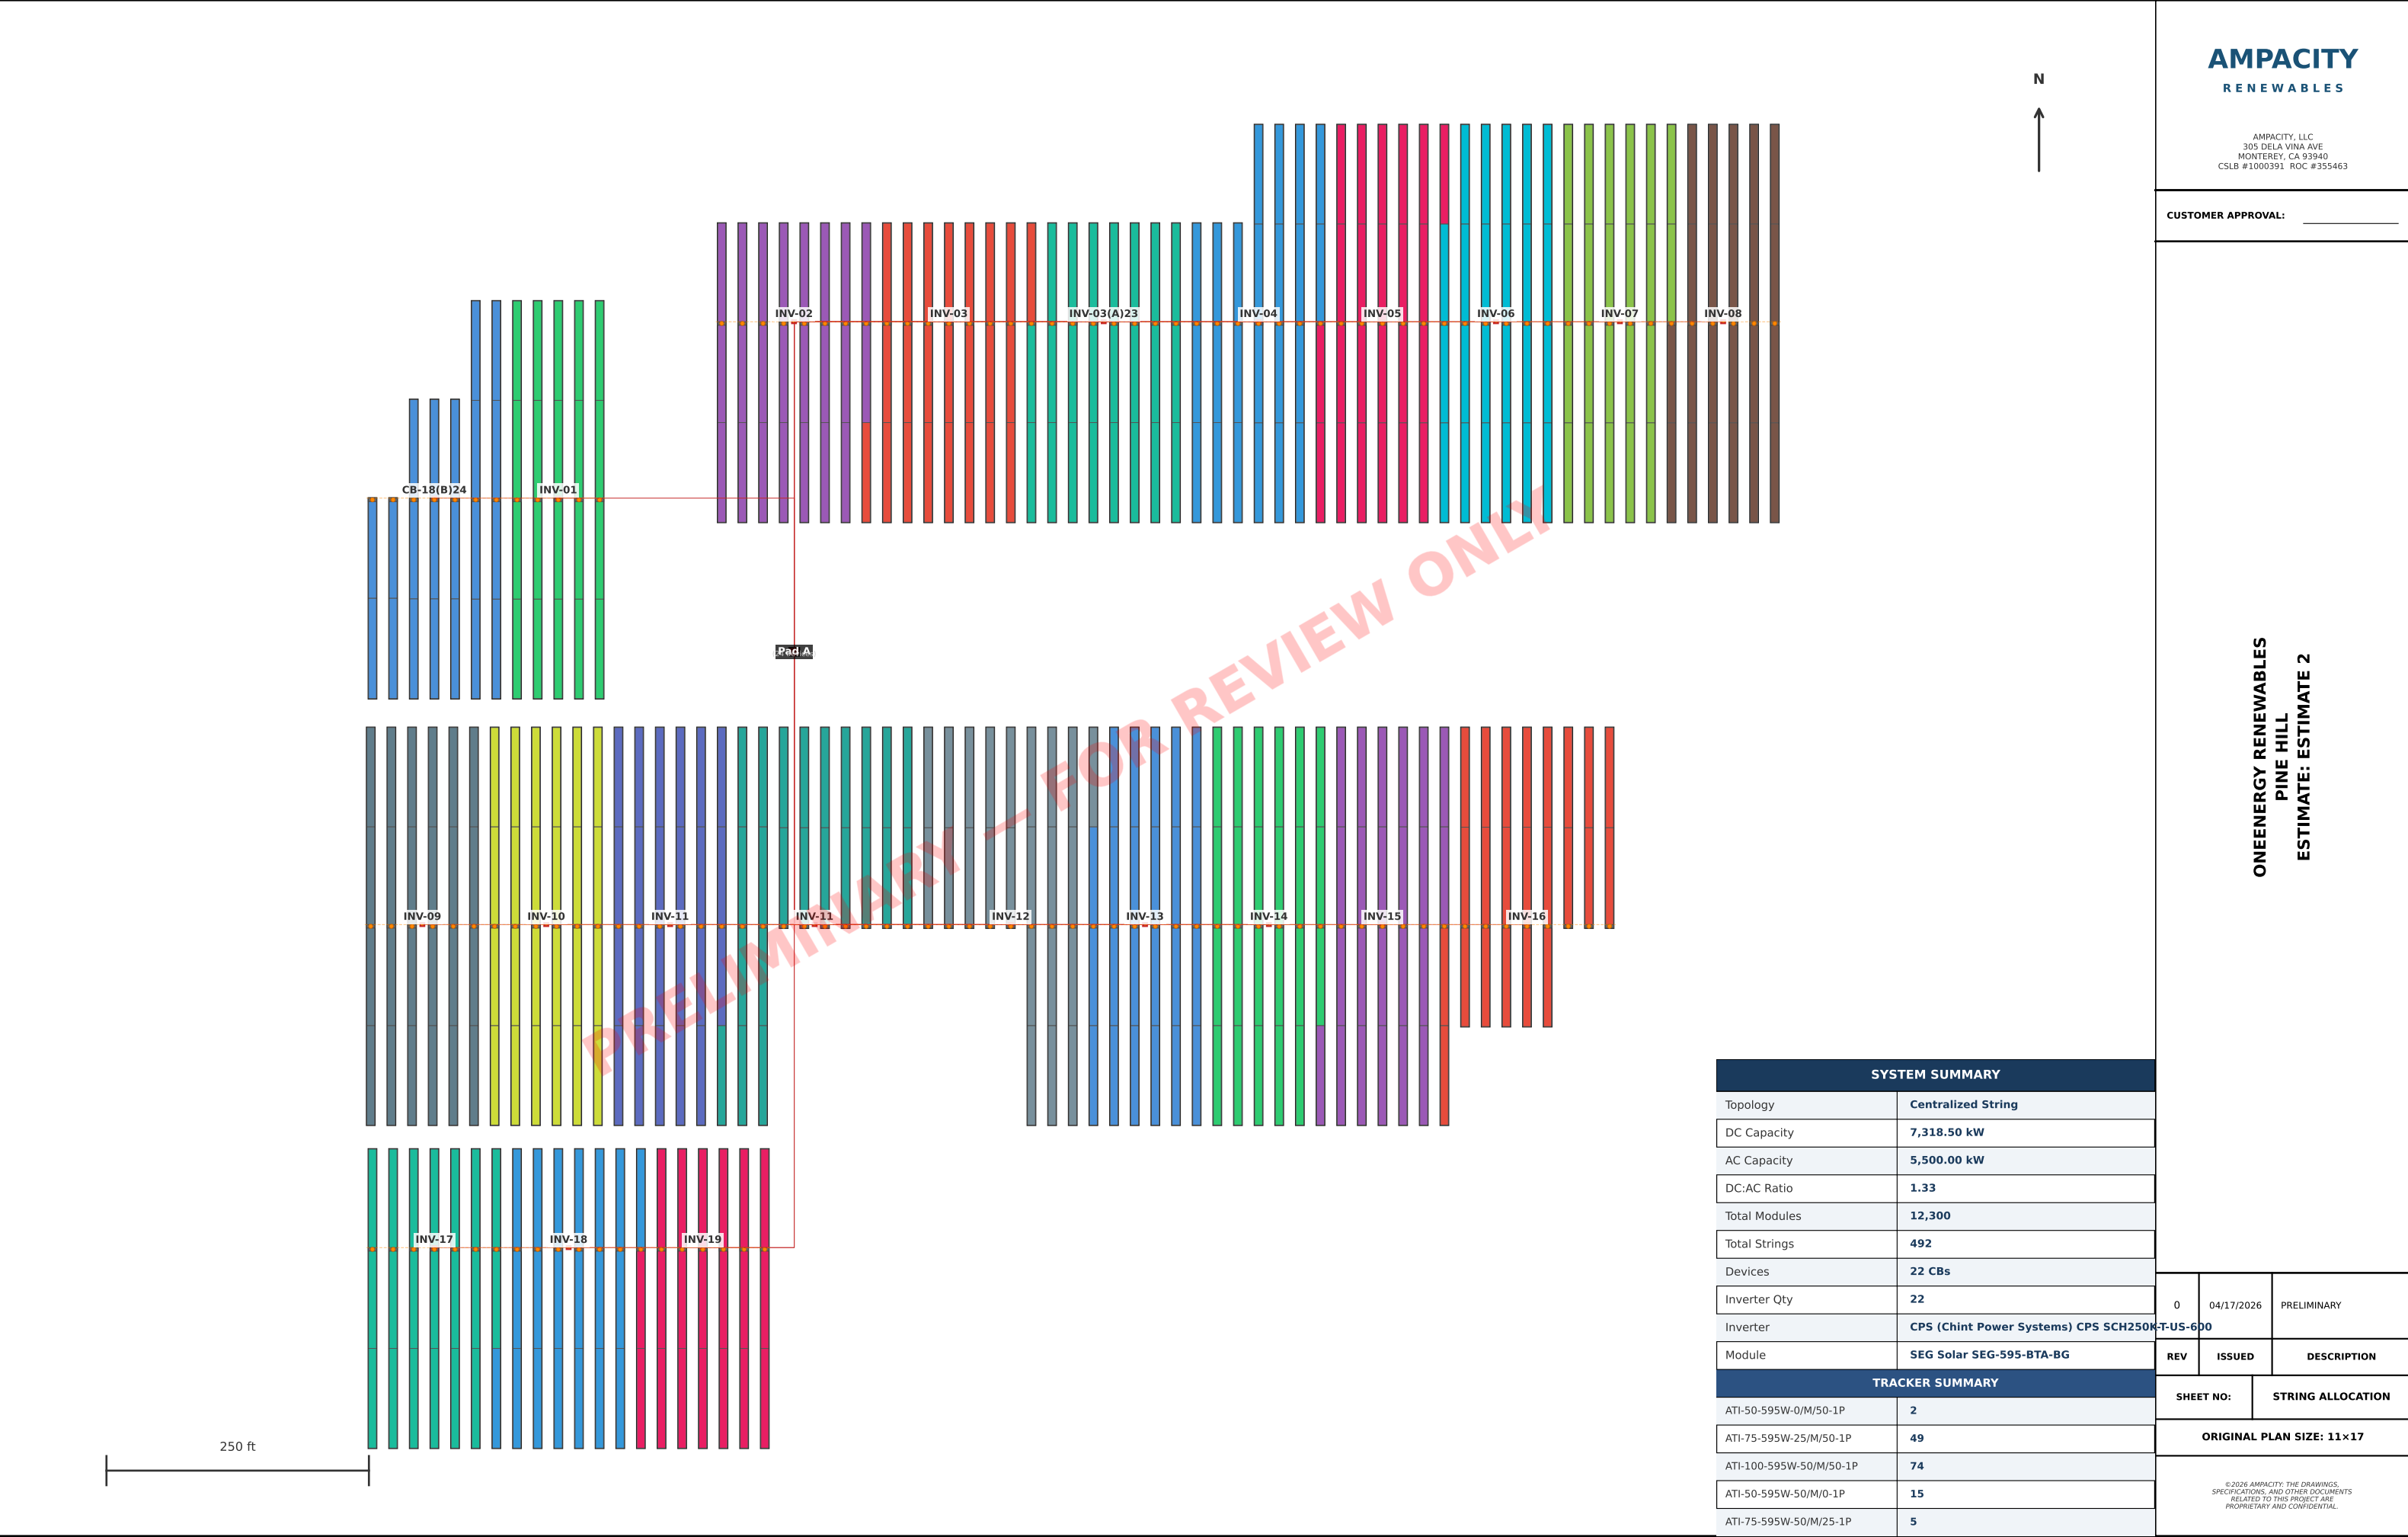

CUSTOMER APPROVAL: _____

ONEENERGY RENEWABLES
PINE HILL
ESTIMATE: ESTIMATE 2

SYSTEM SUMMARY

Topology	Centralized String
DC Capacity	7,318.50 kW
AC Capacity	5,500.00 kW
DC:AC Ratio	1.33
Total Modules	12,300
Total Strings	492
Devices	22 CBs
Inverter Qty	22
Inverter	CPS (Chint Power Systems) CPS SCH250K-T-US-600
Module	SEG Solar SEG-595-BTA-BG

TRACKER SUMMARY

ATI-50-595W-0/M/50-1P	2
ATI-75-595W-25/M/50-1P	49
ATI-100-595W-50/M/50-1P	74
ATI-50-595W-50/M/0-1P	15
ATI-75-595W-50/M/25-1P	5

0	04/17/2026	PRELIMINARY
REV	ISSUED	DESCRIPTION

SHEET NO:	STRING ALLOCATION
-----------	-------------------

ORIGINAL PLAN SIZE: 11×17